
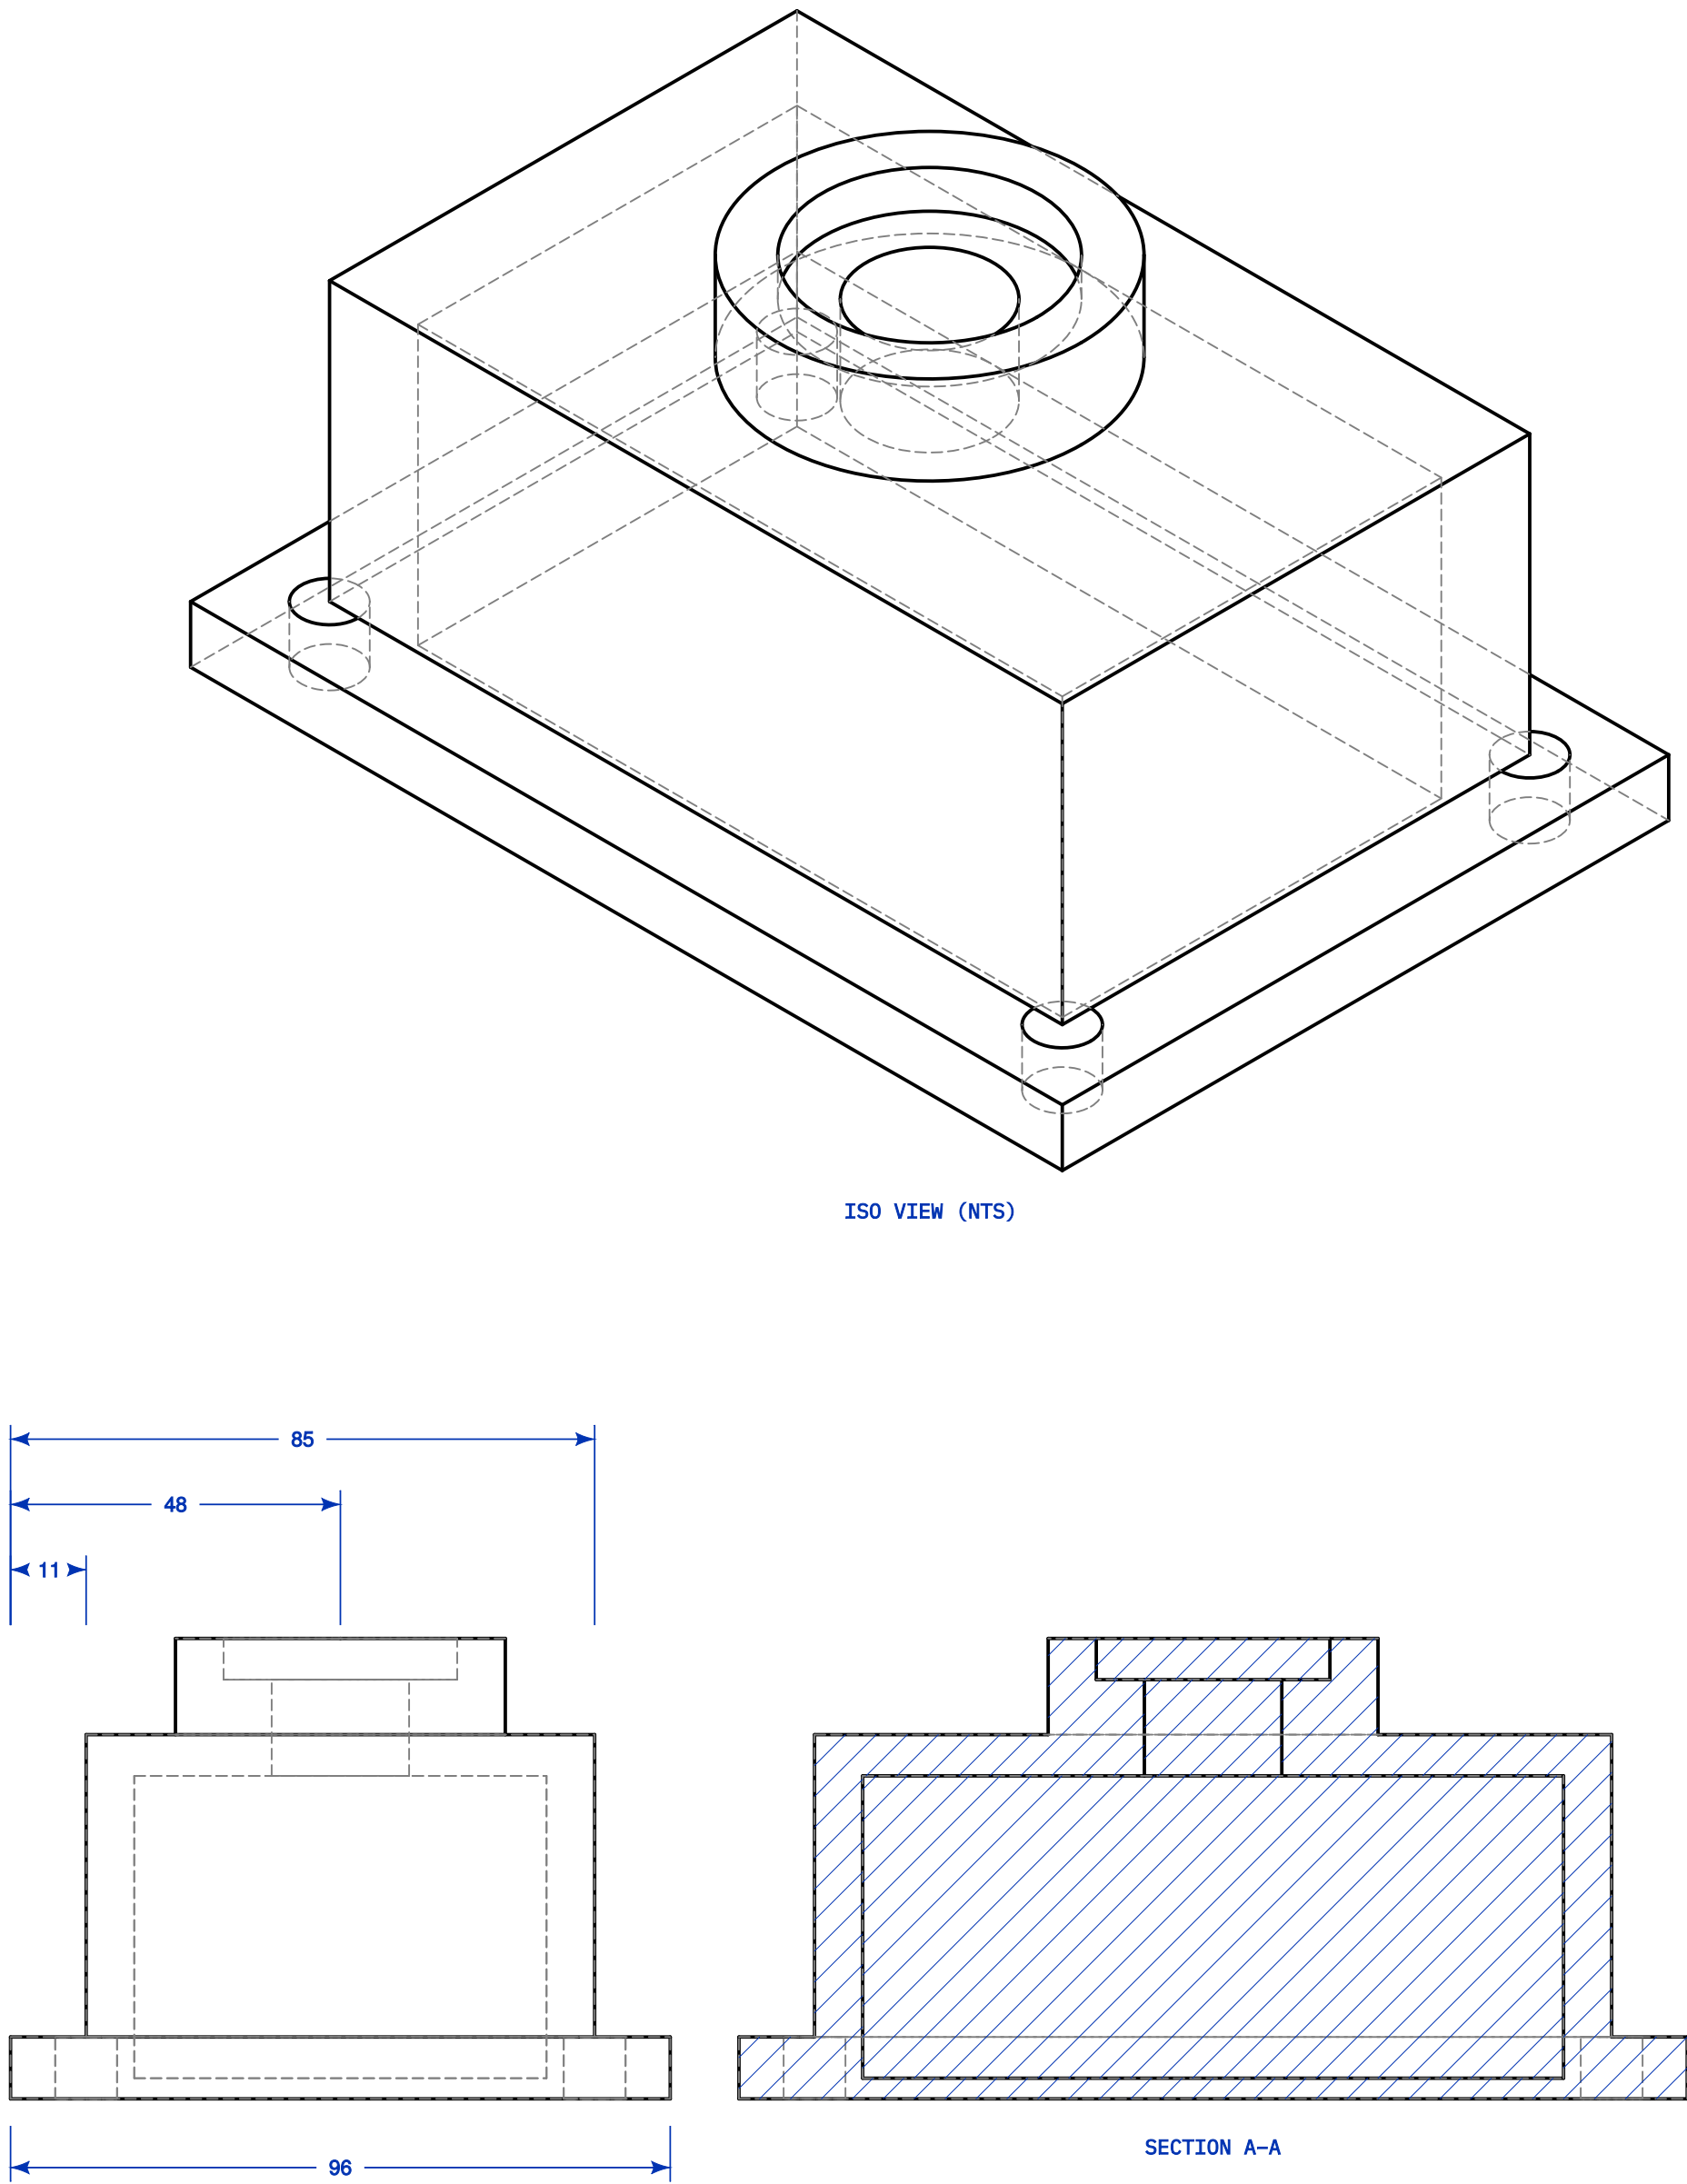


FEATURES
4X DIA 9 THRU ON 116 X 74 RECTANGULAR CENTERS
CENTER BORE DIA 20 THRU
COUNTERBORE DIA 34 X 6 DEEP

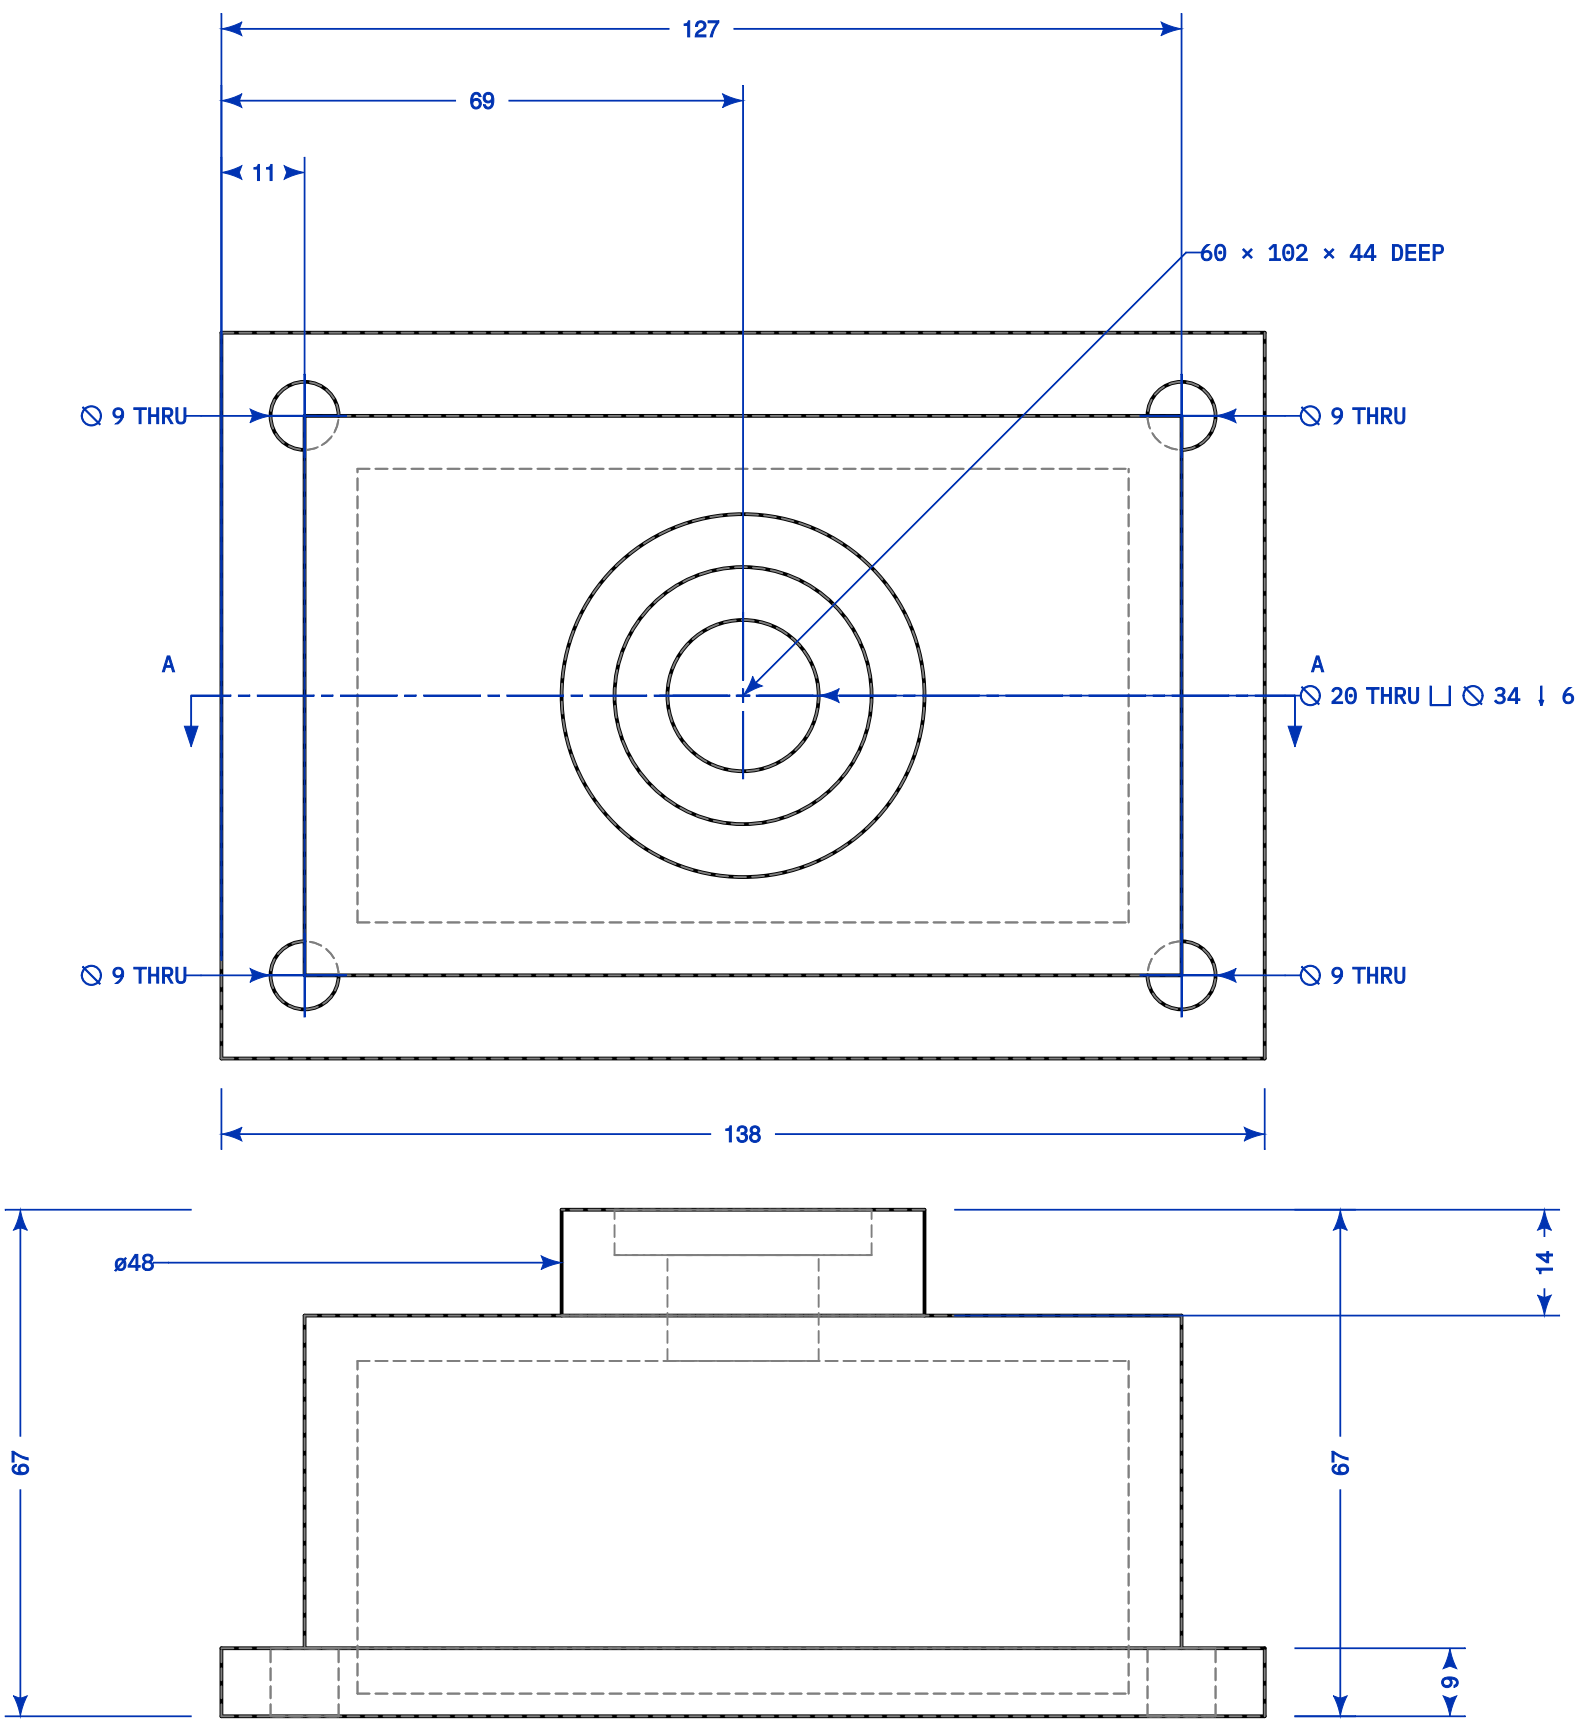

TITLE	Counterbored Flange Housing	DWG NO.	DWG-001	SCALE	1:1	REV.	A
DATE	2024-10-27	DESIGNED BY	draftwright	CHECKED BY		APPROVED BY	